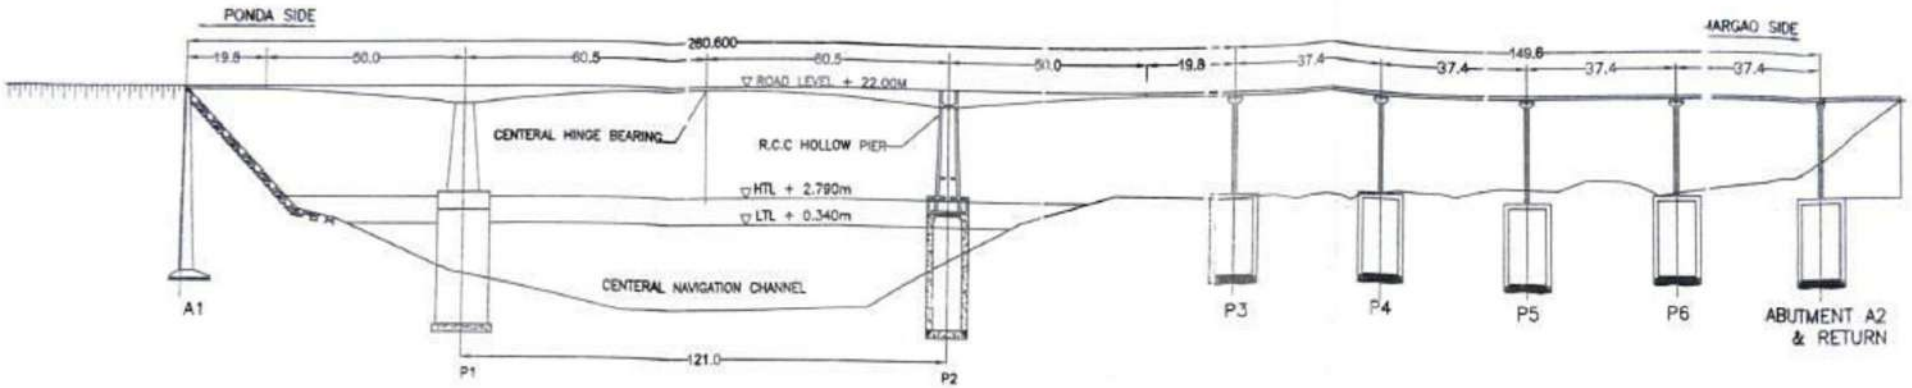

LONGITUDINAL SECTION

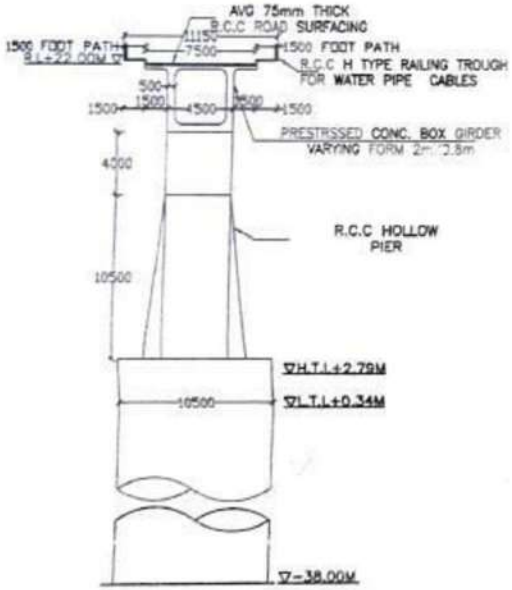

CROSS SECTION AT P1

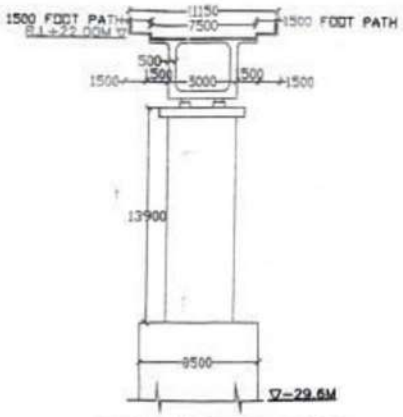

CROSS SECTION AT P5

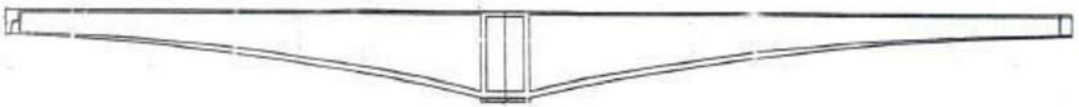

SECTIONAL ELEVATION
(HINGED SPAN BETWEEN P1-P2 & CANTLEVER SPAN BETWEEN A1-P1)

DETAILS OF EXTERNAL CABLES
(HINGED SPAN BETWEEN P1-P2 & CANTLEVER SPAN BETWEEN A1-P1)

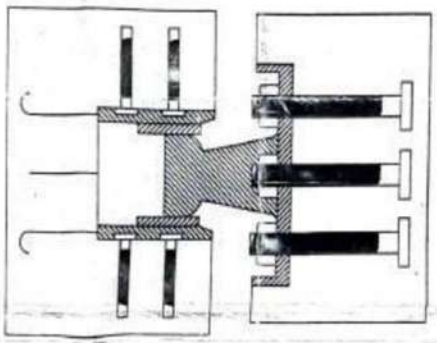

DETAILS OF HINGE

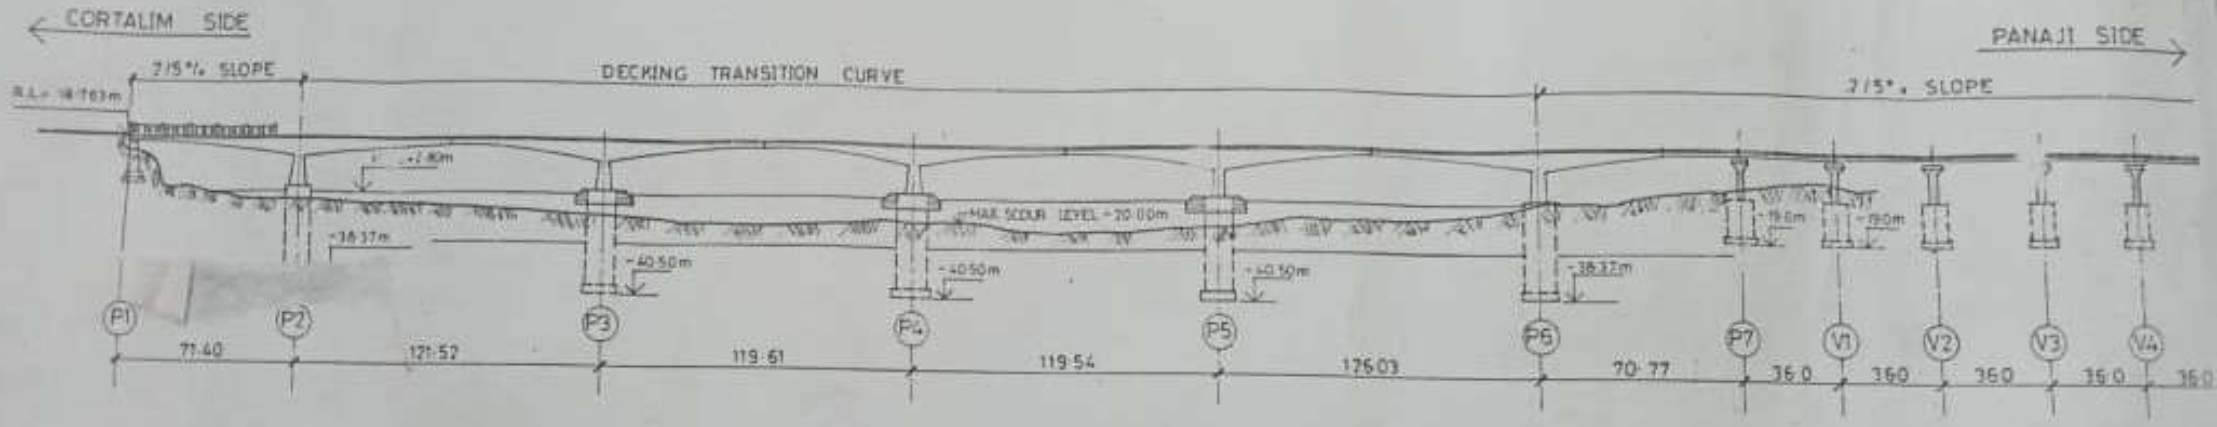

G.A.D. OF ZUARI BRIDGE ON NH 17 GOA

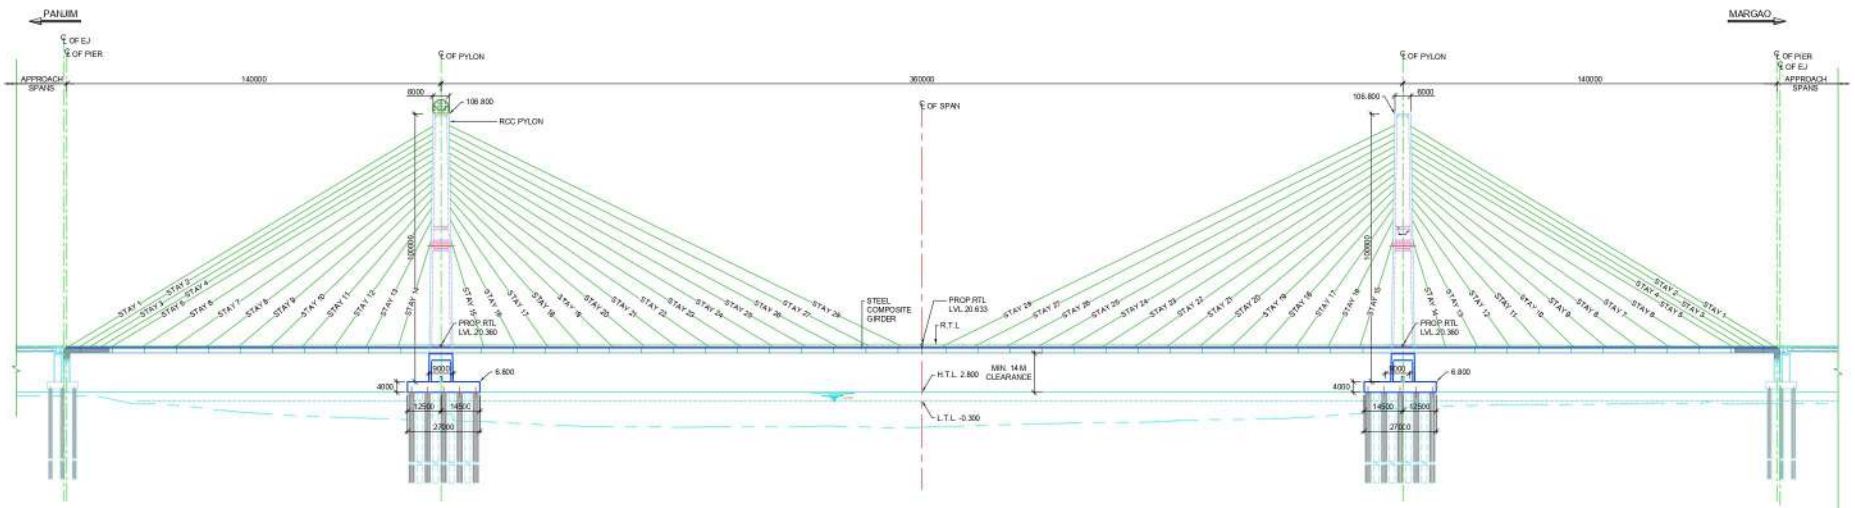

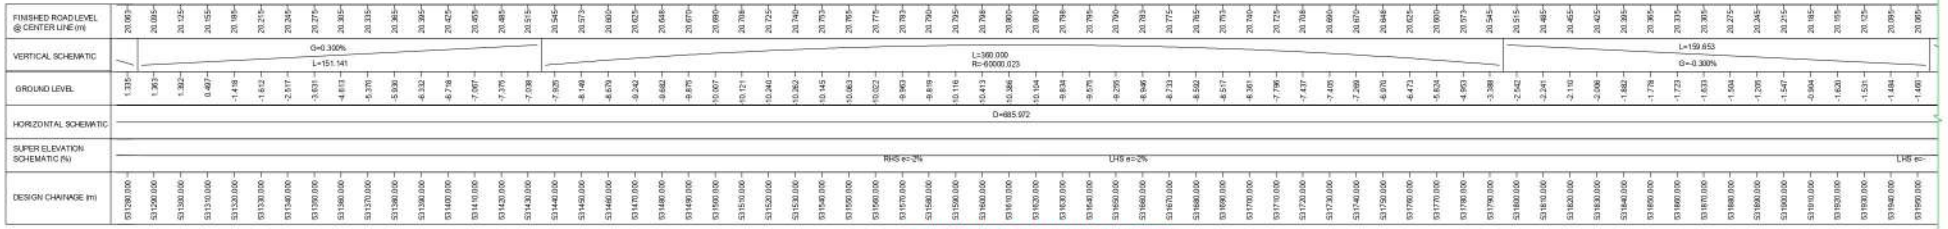

LONGITUDINAL SECTION OF BRIDGE

(SCALE - 1 : 1000)

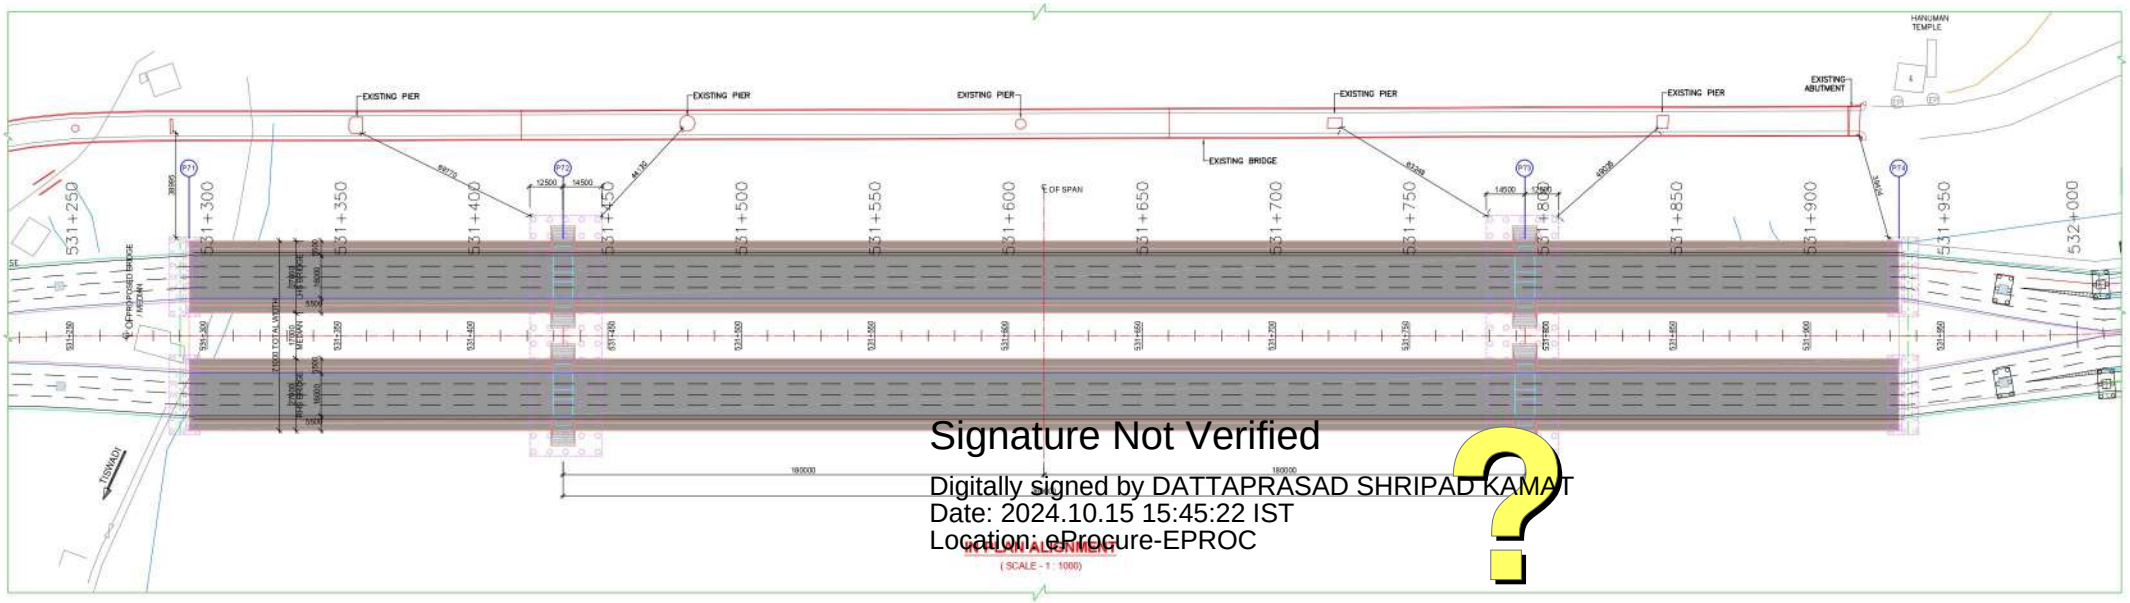

HYDRAULIC ALIGNMENT

(SCALE - 1 : 1000)

Signature Not Verified
Digitally signed by DATTAPRASAD SHRIPAD KAMAT
Date: 2024.10.15 15:45:22 IST
Location: eProcure-EPROC