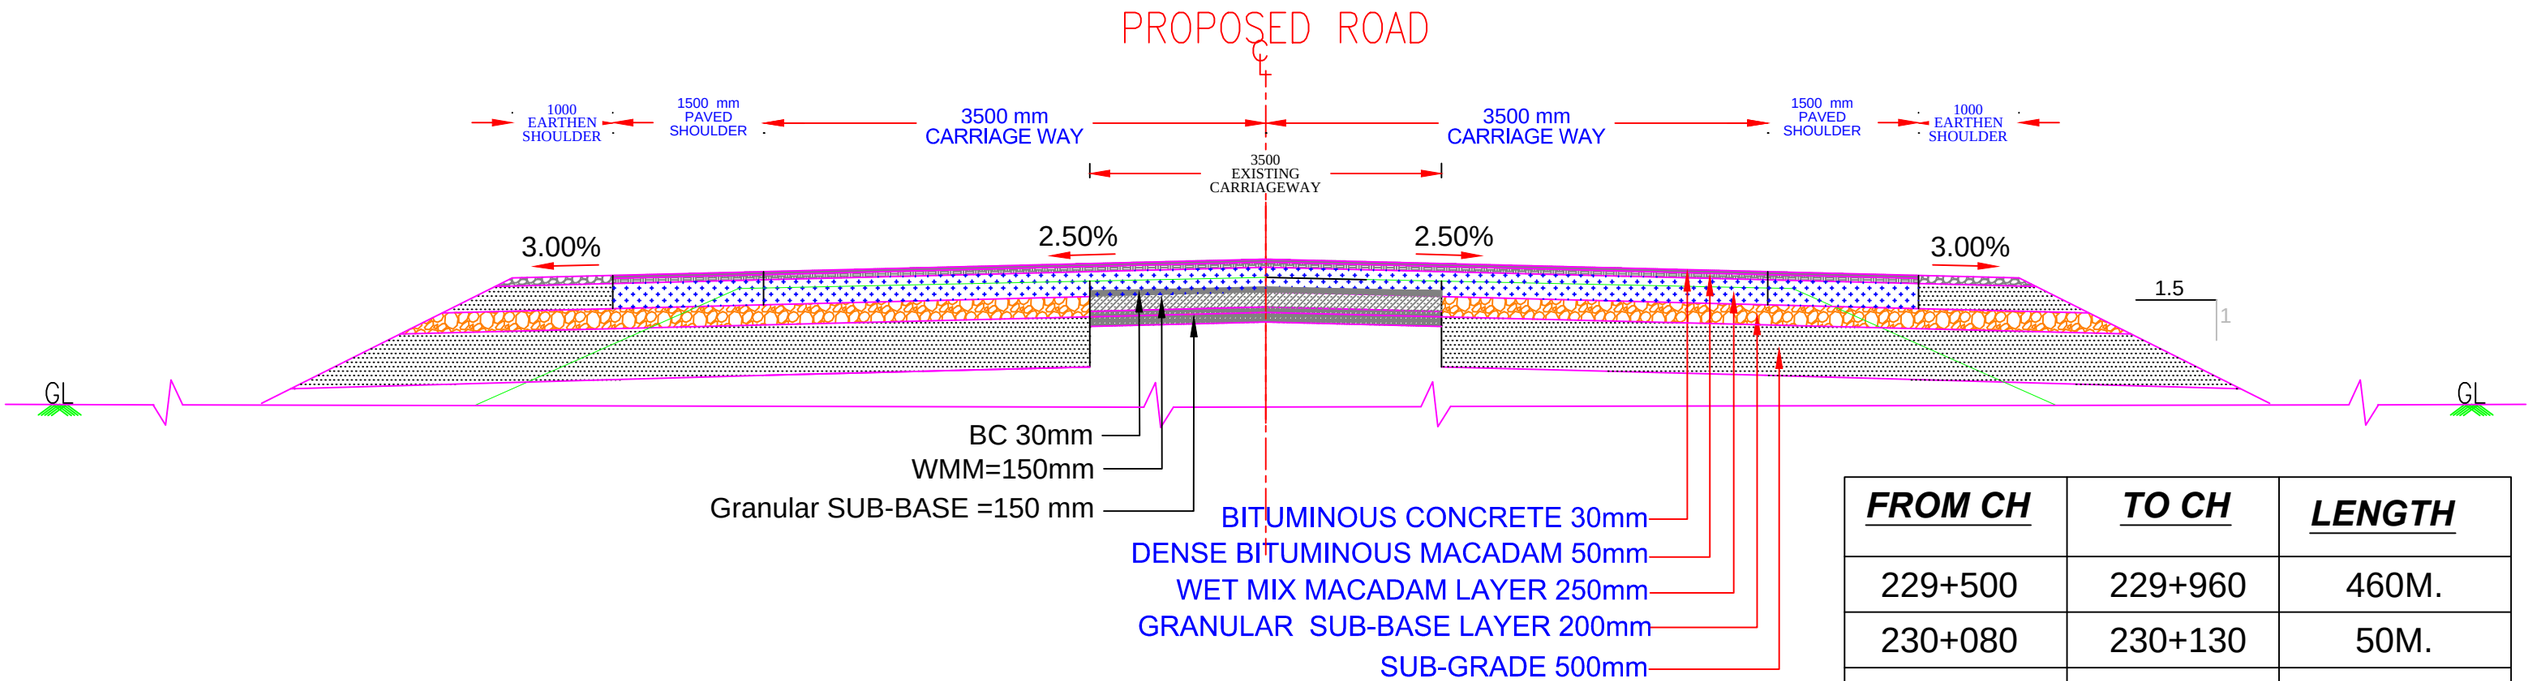

TCS-I : TYPICAL CROSS SECTION
(RECONSTRUCTION OPEN AREA)
2-LANE CARRIAGEWAY WITH PAVED SHOULDER
(AS PER FIG. 2.1, IRC SP 73-2018 (MODIFIED))

FROM CH	***TO CH***	***LENGTH***
229+500	229+960	460M.
230+080	230+130	50M.
230+170	230+300	130M.
248+800	249+000	200M.
249+200	249+430	230M.
250+510	251+630	1120M.
251+760	251+890	130M.
252+100	252+340	240M.
252+390	255+560	3170M.
255+810	256+188	378M.
256+212	256+468	256M.
TOTAL LENGTH		**6364M.**

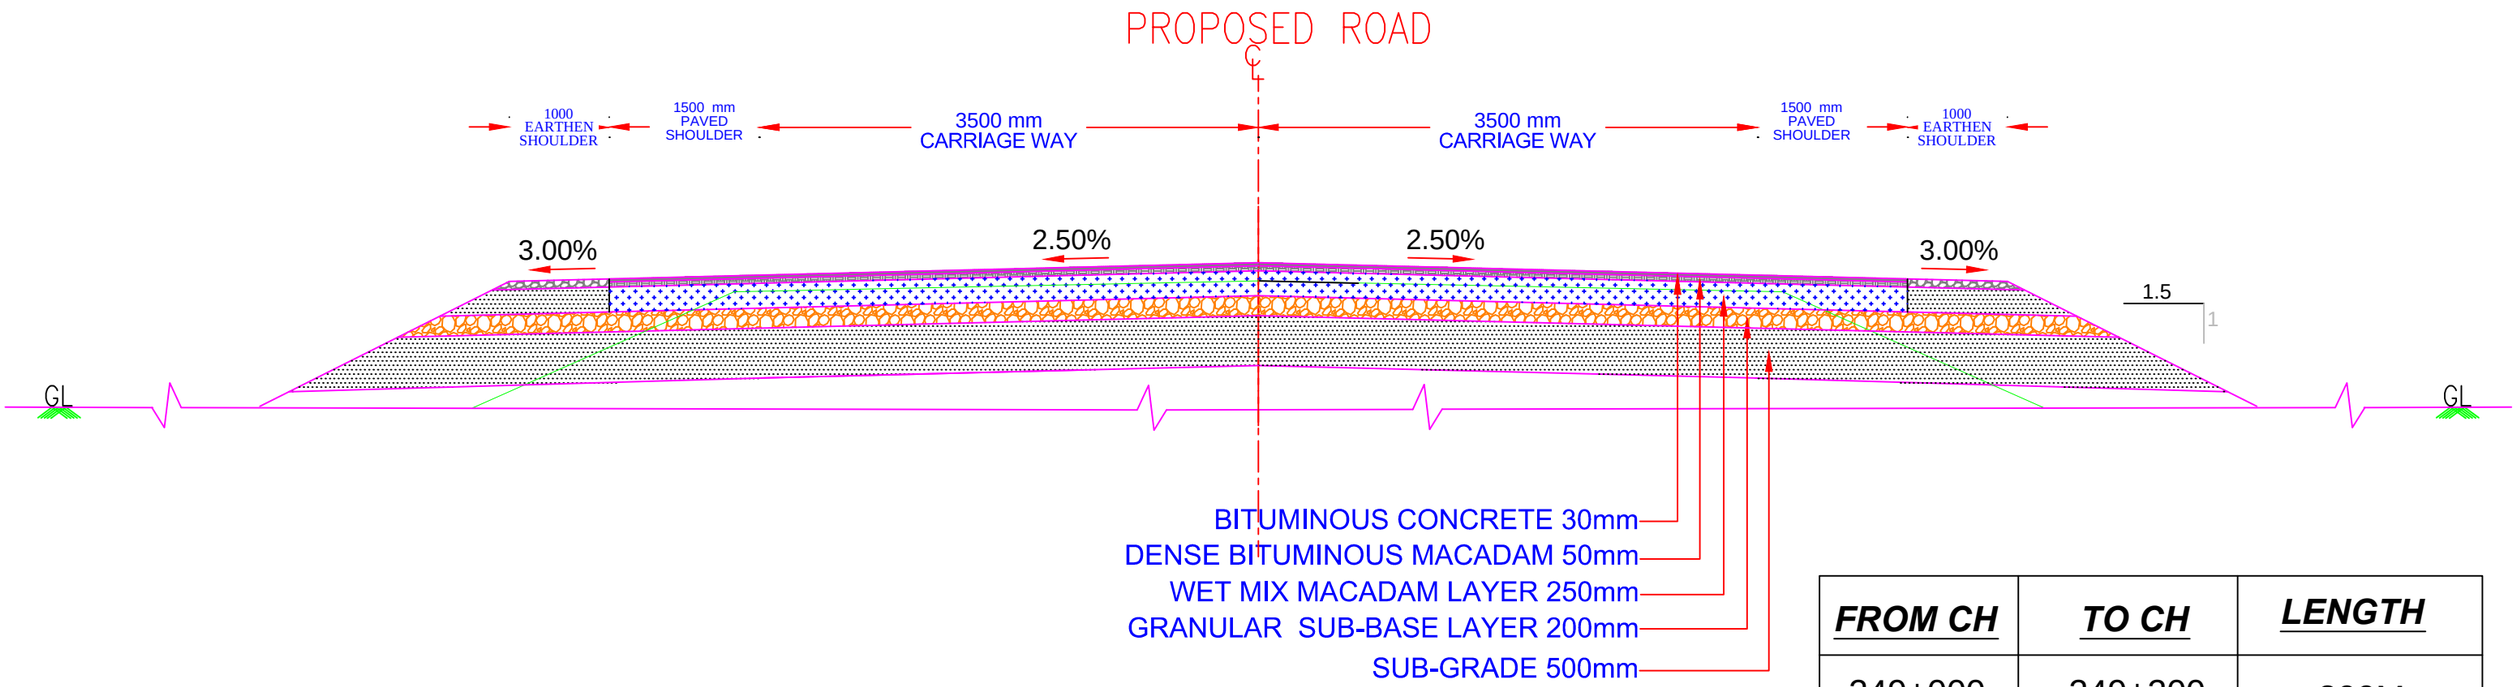

TCS-II: TYPICAL CROSS SECTION
(NEW CONSTRUCTION OPEN AREA)
2-LANE CARRIAGEWAY WITH PAVED SHOULDER
(AS PER FIG. 2.1, IRC SP 73-2018 (MODIFIED))

FROM CH	***TO CH***	***LENGTH***
249+000	249+200	200M.
TOTAL LENGTH		**200M.**

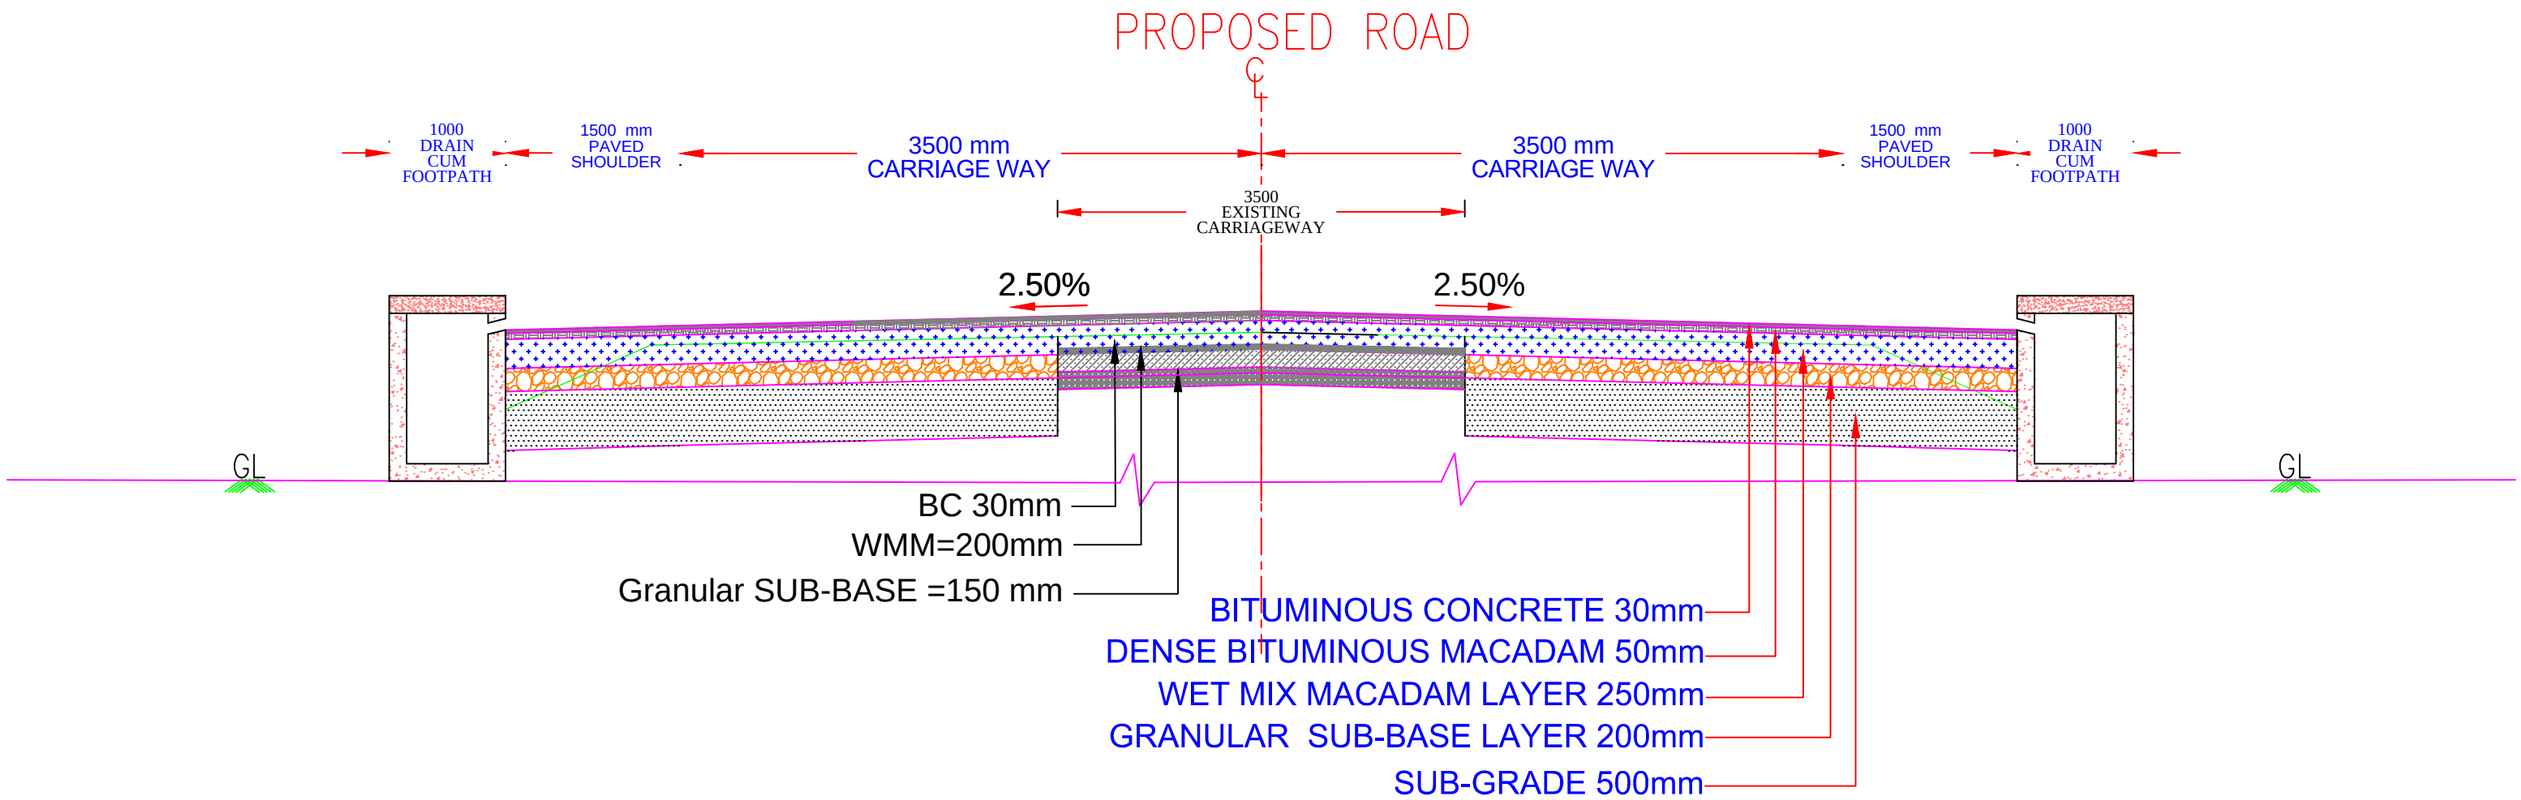

TCS-III : TYPICAL CROSS SECTION
(RECONSTRUCTION BUILT - UP SECTION)
2-LANE CARRIAGEWAY WITH PAVED SHOULDER
(AS PER FIG. 2.1, IRC SP 73-2018 (MODIFIED))

FROM CH	***TO CH***	***LENGTH***
230+300	230+710	410M.
231+500	232+610	1110M.
249+430	250+510	1080M.
TOTAL LENGTH		**2600M.**

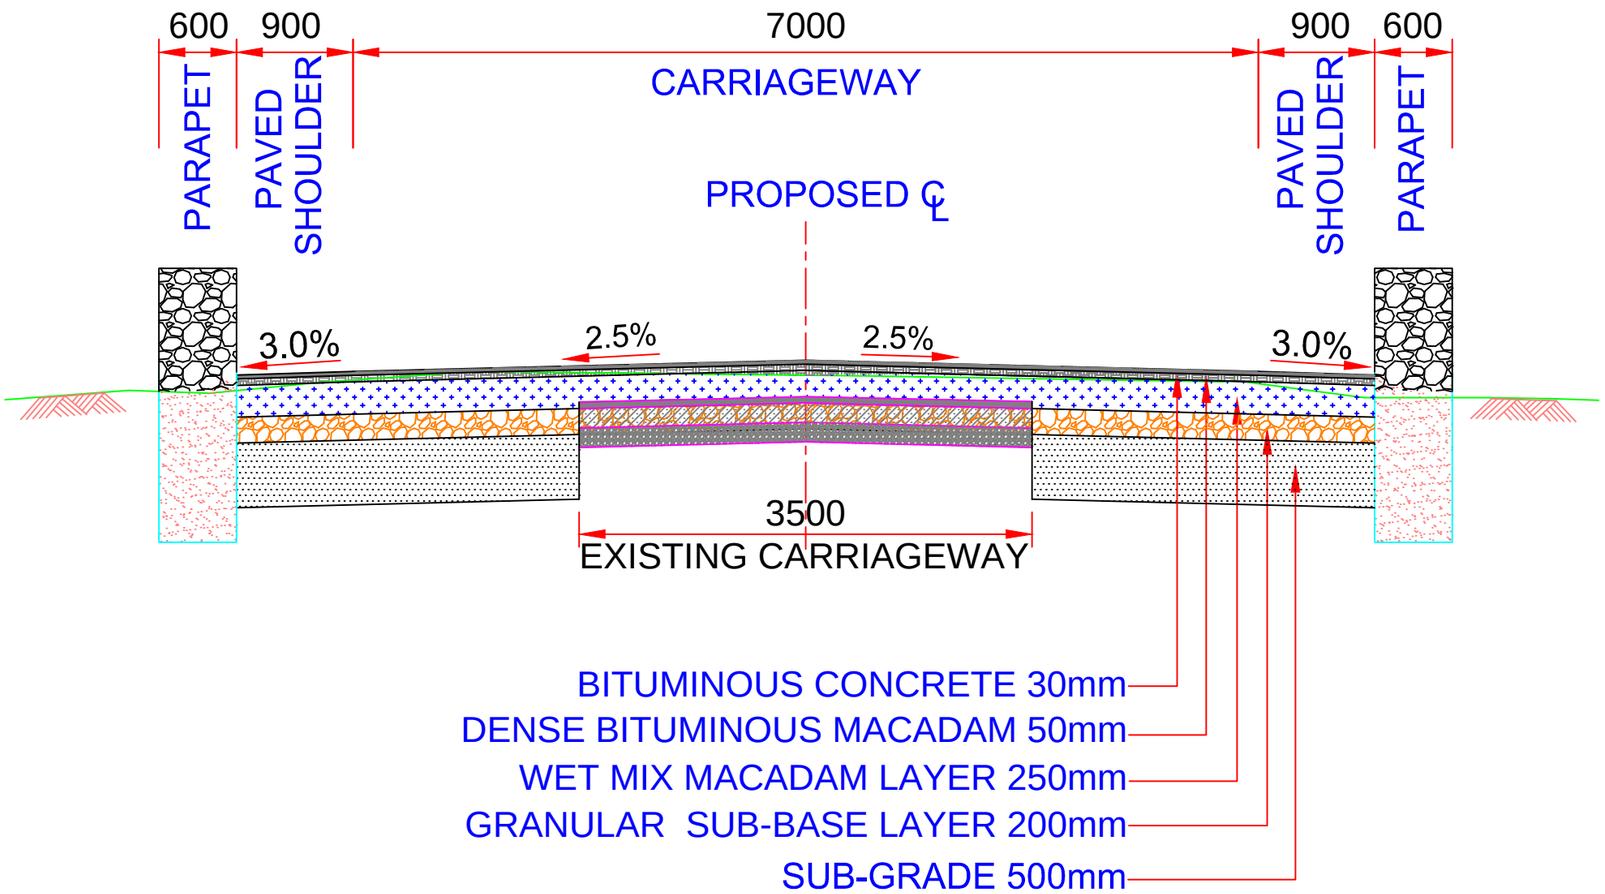

TCS-IV : TYPICAL CROSS SECTION
(RECONSTRUCTION OPEN AREA (HILL))
2-LANE CARRIAGEWAY WITH PAVED SHOULDER
(AS PER FIG. 2.1, IRC SP 73-2018 (MODIFIED))

FROM CH	***TO CH***	***LENGTH***
231+440	231+500	60M.
232+610	232+650	40M.
235+640	235+660	20M.
236+490	236+600	110M.
236+710	236+800	90M.
236+850	236+930	80M.
237+170	237+400	230M.
237+530	237+620	90M.
238+929	238+940	11M.
239+610	239+640	30M.
240+380	240+410	30M.
240+520	240+530	10M.
245+910	246+110	200M.
246+210	246+260	50M.
246+400	246+960	560M.
247+326	247+776	450M.
248+026	248+286	250M.
248+420	248+510	90M.
TOTAL LENGTH		**2411M.**

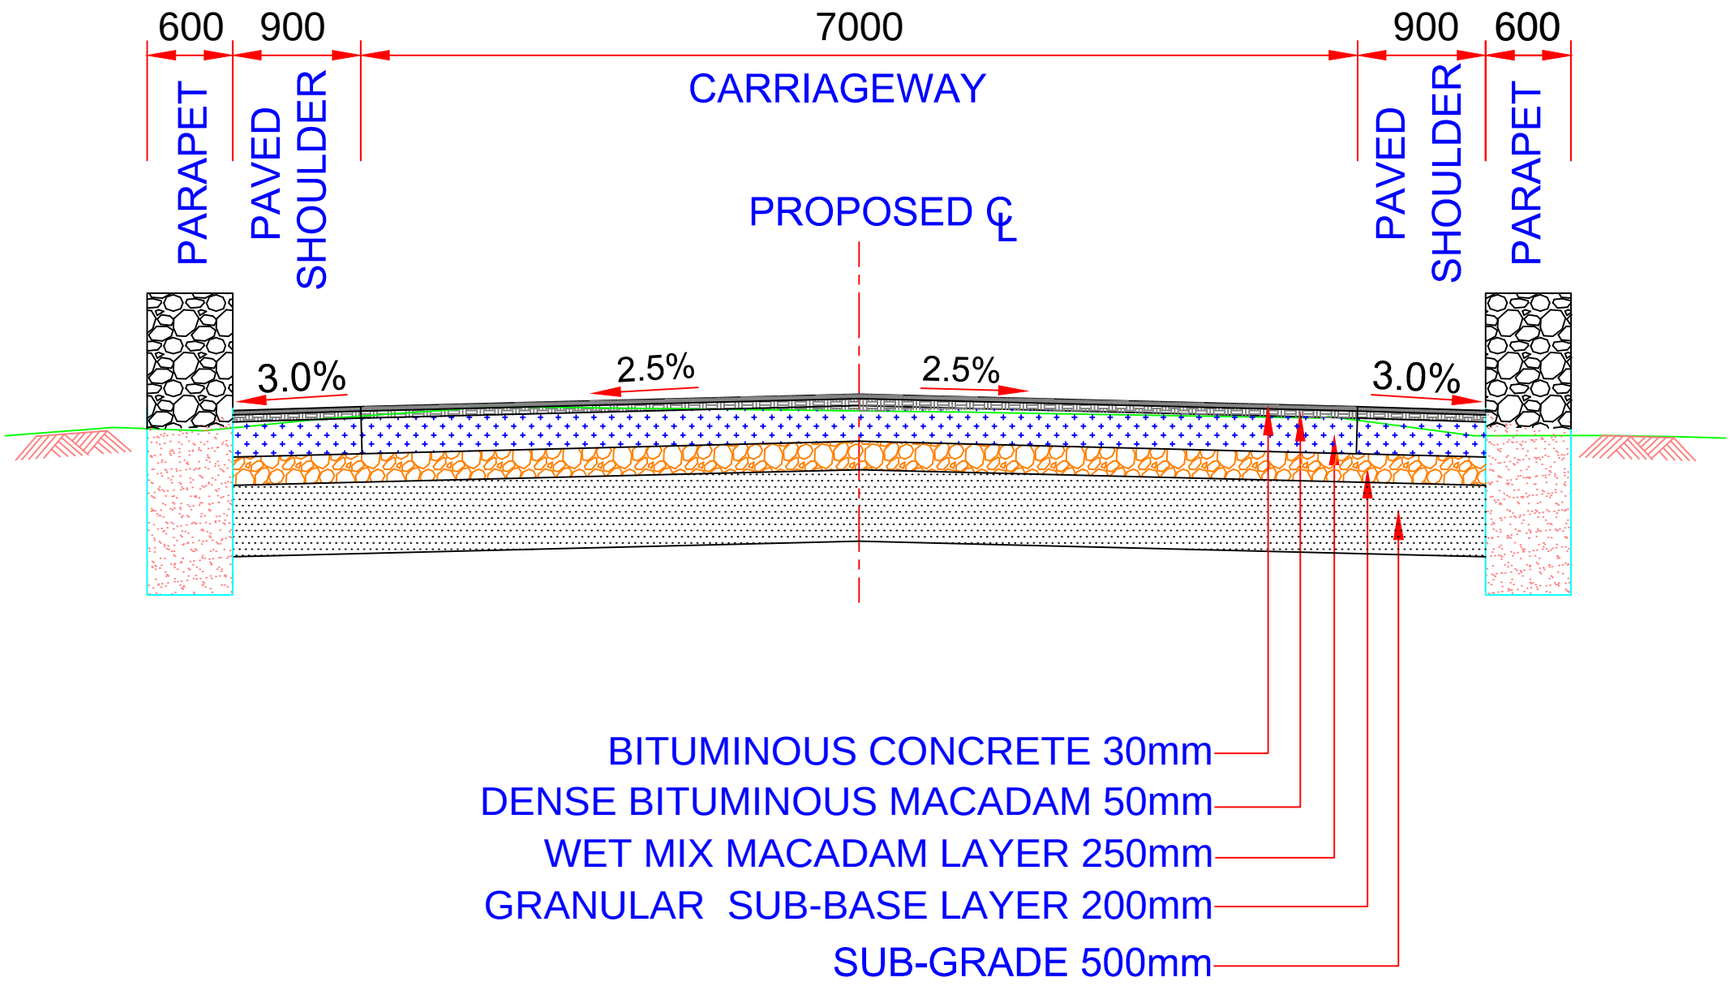

TCS-V : TYPICAL CROSS SECTION
(NEW CONSTRUCTION OPEN AREA (HILL))
2-LANE CARRIAGEWAY WITH PAVED SHOULDER
(AS PER FIG. 2.1, IRC SP 73-2018 (MODIFIED))

FROM CH	***TO CH***	***LENGTH***
230+860	230+959	99M.
232+650	232+670	20M.
233+869	233+880	11M.
233+890	233+940	50M.
233+980	234+120	140M.
234+380	234+400	20M.
237+050	237+100	50M.
237+757	237+867	110M.
238+450	238+600	150M.
239+350	239+360	10M.
243+345	243+365	20M.
244+575	244+595	10M.
247+110	247+292	182M.
TOTAL LENGTH		**882M.**

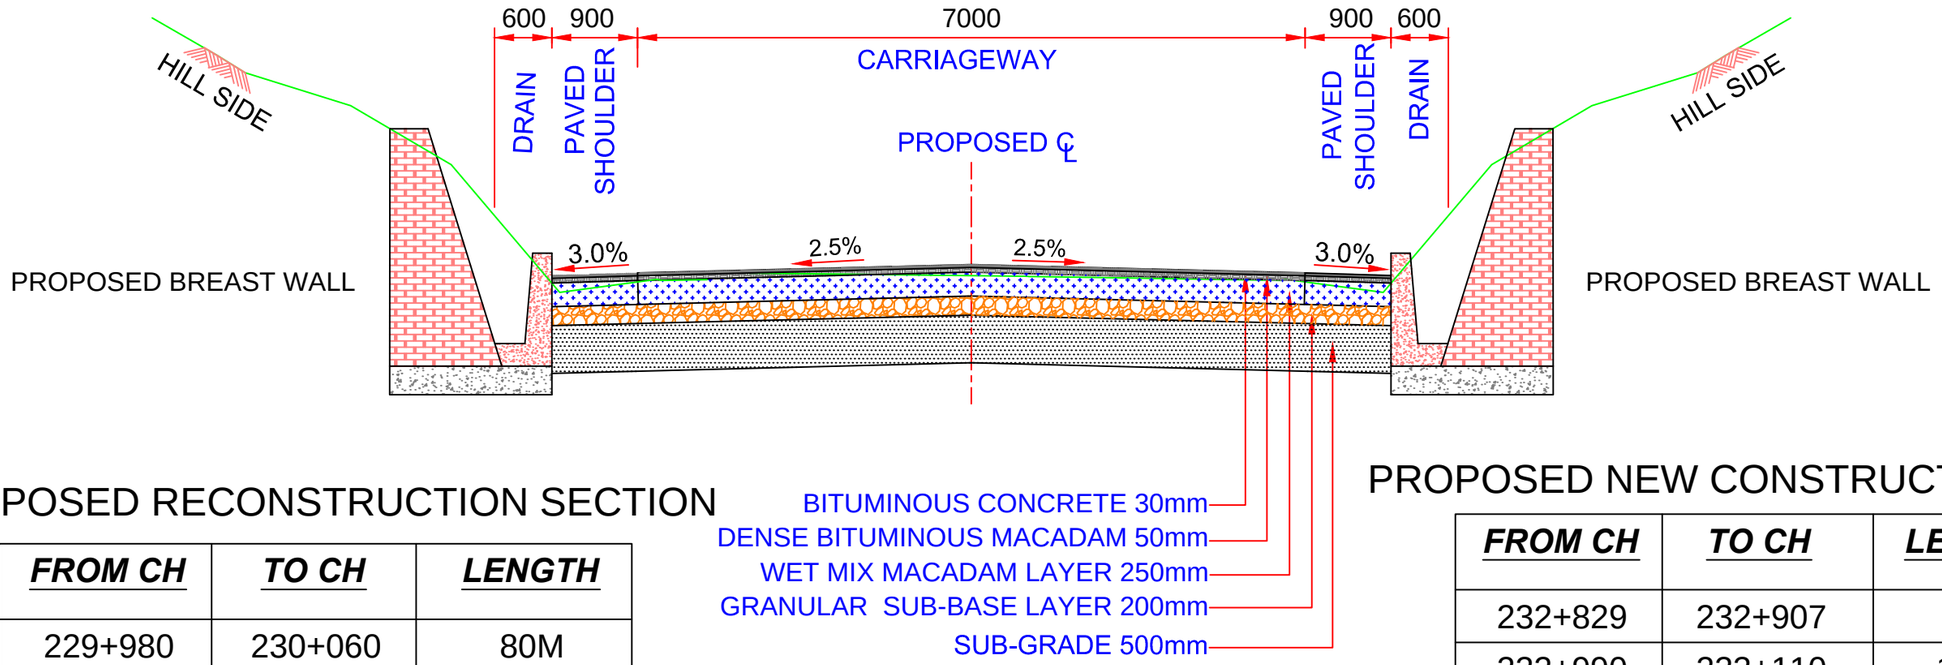

TCS-VI : TYPICAL CROSS SECTION
(BOTH SIDE HILL VARRIES)
2-LANE CARRIAGEWAY WITH PAVED SHOULDER
(AS PER MORT&H SPECIFICATION (MODIFIED))

PROPOSED RECONSTRUCTION SECTION

FROM CH	***TO CH***	***LENGTH***
229+980	230+060	80M
233+110	233+310	200M
233+420	233+490	70M
237+400	237+430	30M
237+450	237+460	10M
237+490	237+500	10M
240+550	240+610	60M
240+960	241+417	457M
246+270	246+400	130M
248+530	248+650	120M
TOTAL LENGTH		**1167M.**

PROPOSED NEW CONSTRUCTION SECTION

FROM CH	***TO CH***	***LENGTH***
232+829	232+907	78M.
232+990	233+110	120M.
233+580	233+619	39M.
233+688	233+804	116M.
235+900	235+930	30M.
235+950	235+990	40M.
236+020	236+040	20M.
236+630	236+660	30M.
237+110	237+150	40M.
237+670	237+690	20M.
241+516	241+630	114M.
241+930	242+040	110M.
243+435	243+565	130M.
243+975	243+985	10M.
244+045	244+075	30M.
244+505	244+545	40M.
244+850	244+990	140M.
TOTAL LENGTH		**1107M.**

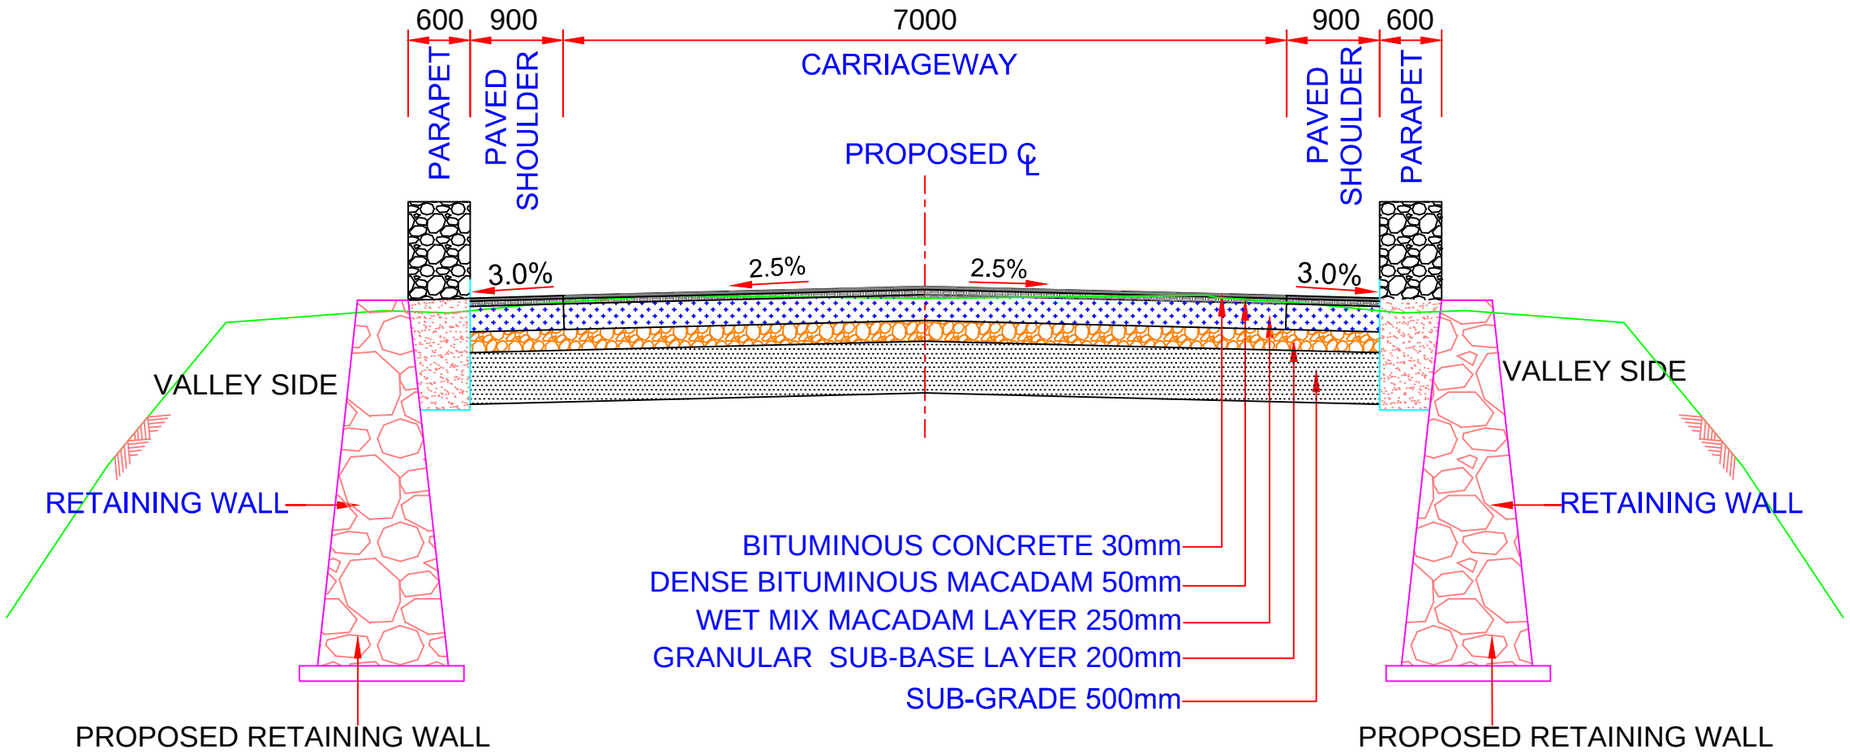

TCS-VII : TYPICAL CROSS SECTION
(BOTH SIDE VALLEY VARRIES)
2-LANE CARRIAGEWAY WITH PAVED SHOULDER
(AS PER MORT&H SPECIFICATION (MODIFIED))

PROPOSED RECONSTRUCTION SECTION

FROM CH	***TO CH***	***LENGTH***
234+660	234+700	40M.
TOTAL LENGTH		**40M.**

PROPOSED NEW CONSTRUCTION SECTION

FROM CH	***TO CH***	***LENGTH***
245+280	245+290	10M.
TOTAL LENGTH		**10M.**

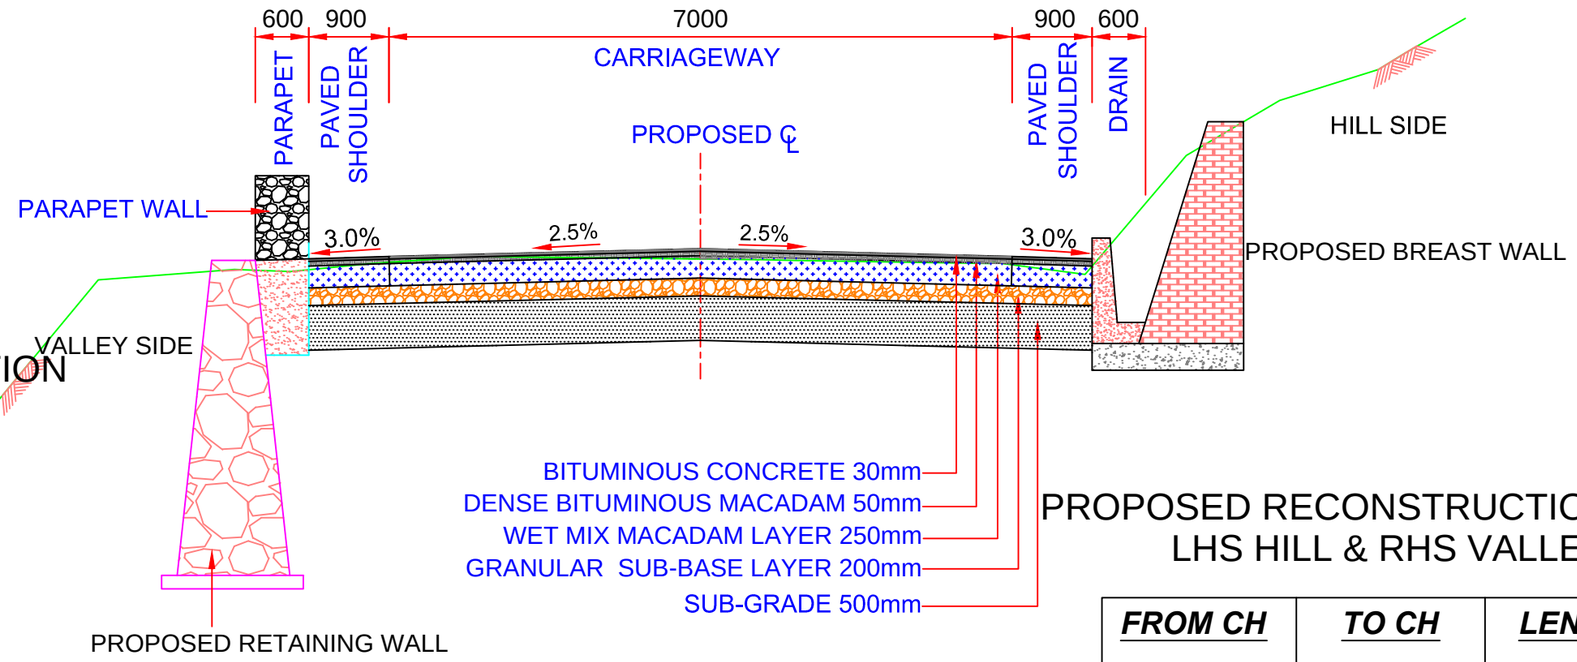

TCS-VIII : TYPICAL CROSS SECTION
(ONE SIDE HILL ANOTHER SIDE VALLEY VARRIES)
2-LANE CARRIAGEWAY WITH PAVED SHOULDER
(AS PER MORT&H SPECIFICATION (MODIFIED))

PROPOSED RECONSTRUCTION SECTION RHS HILL & LHS VALLEY

FROM CH	***TO CH***	***LENGTH***
239+700	239+730	30M.
239+990	240+030	40M.
240+260	240+280	20M.
TOTAL LENGTH		**90M.**

PROPOSED NEW CONSTRUCTION SECTION RHS HILL & LHS VALLEY

FROM CH	***TO CH***	***LENGTH***
238+610	238+632	22M.
238+700	238+730	30M.
239+310	239+350	40M.
241+910	241+930	20M.
243+565	243+575	10M.
244+185	244+215	30M.
244+235	244+285	50M.
244+390	244+415	20M.
TOTAL LENGTH		**222M.**

PROPOSED RECONSTRUCTION SECTION LHS HILL & RHS VALLEY

FROM CH	***TO CH***	***LENGTH***
235+320	235+460	140M.
235+500	235+540	40M.
TOTAL LENGTH		**180M.**

PROPOSED NEW CONSTRUCTION SECTION LHS HILL

FROM CH	TO CH	LENGTH
232+700	232+759	59M.
232+972	232+990	18M.
235+930	235+950	20M.
235+990	236+020	30M.
236+040	236+100	60M.
236+660	236+690	30M.
237+620	237+670	50M.
248+650	248+800	150M.
TOTAL LENGTH		**417M.**

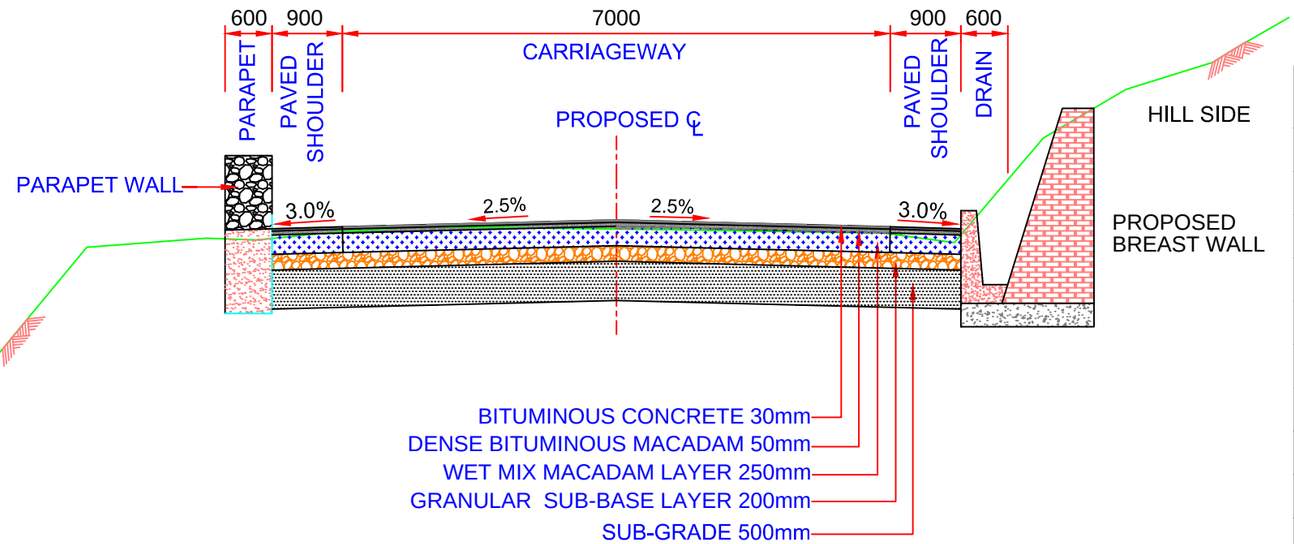

TCS-IX : TYPICAL CROSS SECTION
(ONE SIDE HILL VARRIES)
2-LANE CARRIAGEWAY WITH PAVED SHOULDER
(AS PER MORT&H SPECIFICATION (MODIFIED))

PROPOSED NEW CONSTRUCTION SECTION RHS HILL

FROM CH	TO CH	LENGTH
231+025	231+300	275M.
233+940	233+980	40M.
237+100	237+110	10M.
242+040	242+438	398M.
242+689	242+832	143M.
243+365	243+435	70M.
243+985	244+045	60M.
244+075	244+105	30M.
244+145	244+185	40M.
244+285	244+345	60M.
244+415	244+505	90M.
244+545	244+575	30M.
244+820	244+850	30M.
244+990	245+140	150M.
TOTAL LENGTH		**1426M.**

PROPOSED RECONSTRUCTION SECTION LHS HILL

FROM CH	TO CH	LENGTH
229+960	229+980	20M.
230+060	230+080	20M.
233+310	233+420	110M.
233+490	233+580	90M.
235+660	235+900	240M.
236+930	237+050	120M.
237+150	237+170	20M.
237+430	237+450	20M.
237+460	237+490	30M.
237+500	237+530	30M.
246+260	246+270	10M.
248+510	248+530	20M.
TOTAL LENGTH		**730M.**

PROPOSED RECONSTRUCTION SECTION RHS HILL

FROM CH	TO CH	LENGTH
231+300	231+440	140M.
239+360	239+610	250M.
240+280	240+380	100M.
240+410	240+520	110M.
240+530	240+550	20M.
240+610	240+960	350M.
252+340	252+390	50M.
TOTAL LENGTH		**1020M.**

PROPOSED NEW CONSTRUCTION SECTION LHS VALLEY

FROM CH	TO CH	LENGTH
234+468	234+495	27M
234+645	234+660	15M
238+600	238+610	10M
238+730	238+859	129M
239+110	239+310	200M
241+770	241+910	140M
242+649	242+689	40M
243+575	243+780	205M
243+945	243+975	30M
244+105	244+145	40M
244+215	244+235	20M
244+345	244+395	50M
244+690	244+820	130M
245+140	245+280	140M
246+960	247+110	150M
TOTAL LENGTH		**1326M.**

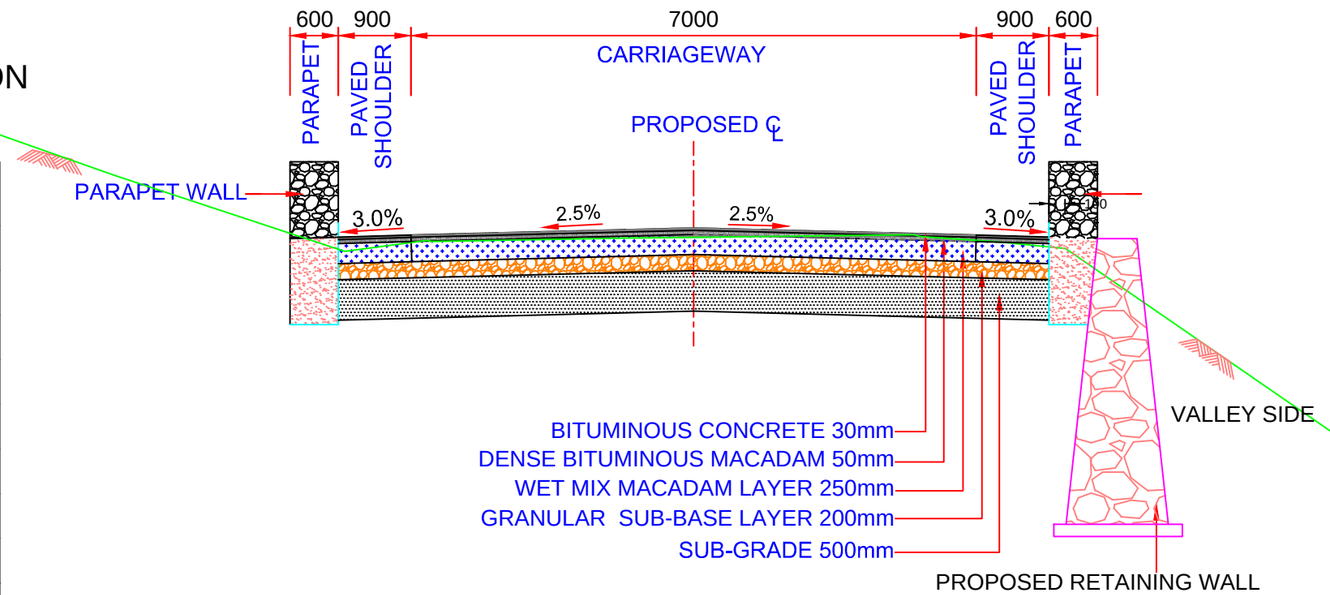

TCS-X : TYPICAL CROSS SECTION
(ONE SIDE VALLEY VARRIES)
2-LANE CARRIAGEWAY WITH PAVED SHOULDER
(AS PER MORT&H SPECIFICATION (MODIFIED))

PROPOSED RECONSTRUCTION SECTION LHS VALLEY

FROM CH	TO CH	LENGTH
239+640	239+680	40M.
239+730	239+990	260M.
240+030	240+260	230M.
247+776	248+006	230M.
TOTAL LENGTH		**760M.**

PROPOSED RECONSTRUCTION SECTION RHS VALLEY

FROM CH	TO CH	LENGTH
230+130	230+170	40M.
230+710	230+860	150M.
234+120	234+380	260M.
234+700	235+320	620M.
235+460	235+500	40M.
235+540	235+640	100M.
236+100	236+490	390M.
236+800	236+850	50M.
237+921	238+450	529M.
238+940	239+086	146M.
245+380	245+910	530M.
246+110	246+210	100M.
248+006	248+026	20M.
248+340	248+420	80M.
251+630	251+760	130M.
251+890	252+100	210M.
255+560	255+810	250M.
TOTAL LENGTH		**3645M.**

PROPOSED NEW CONSTRUCTION SECTION RHS VALLEY

FROM CH	TO CH	LENGTH
232+670	232+700	30M.
233+880	233+890	10M.
236+600	236+630	30M.
236+690	236+710	20M.
245+290	245+380	90M.
TOTAL LENGTH		**180M.**

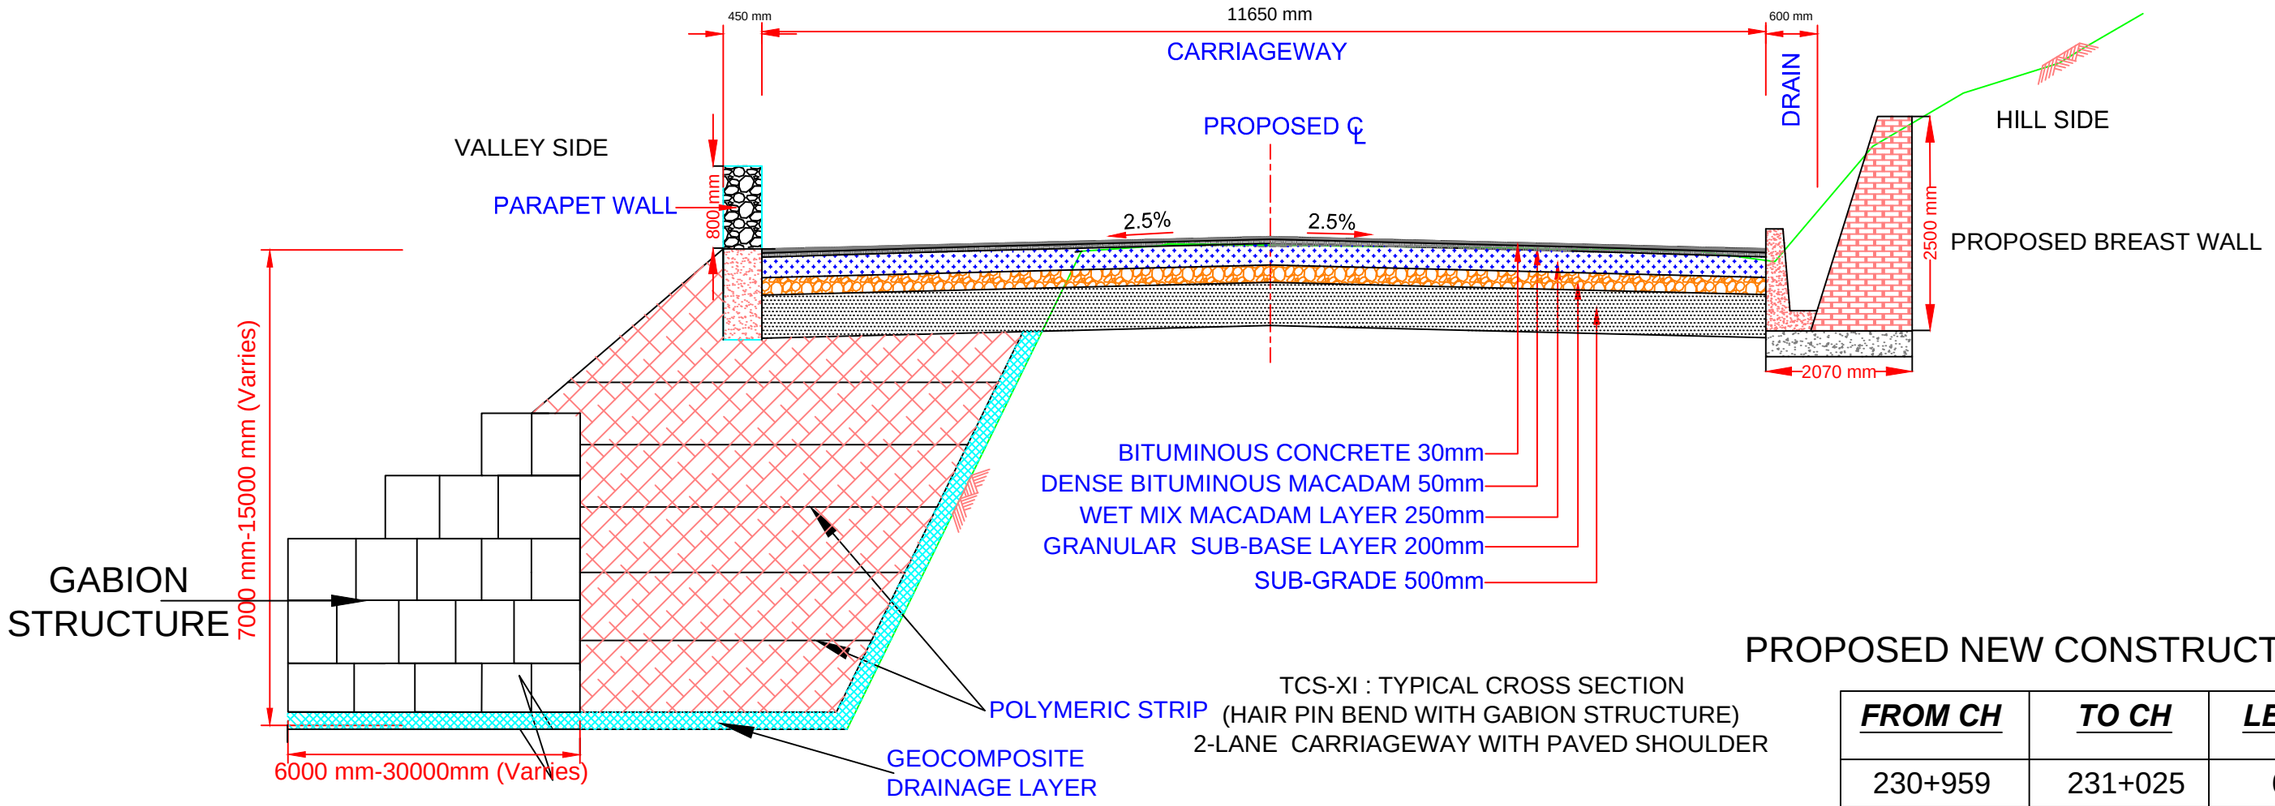

TCS-XI : TYPICAL CROSS SECTION
(HAIR PIN BEND WITH GABION STRUCTURE)
2-LANE CARRIAGEWAY WITH PAVED SHOULDER

PROPOSED RECONSTRUCTION SECTION

FROM CH	***TO CH***	***LENGTH***
238+859	238+929	70M.
TOTAL LENGTH		**70M.**

PROPOSED NEW CONSTRUCTION SECTION

FROM CH	***TO CH***	***LENGTH***
230+959	231+025	66M.
232+759	232+829	70M.
232+907	232+972	65M.
233+619	233+688	69M.
233+804	233+869	65M.
234+400	234+468	68M.
237+690	237+757	67M.
237+867	237+921	54M.
238+632	238+700	68M.
241+417	241+516	99M.
TOTAL LENGTH		**691M.**